


GENERAL PLAN
OF
LOTS 14183-14608 CHARLESHILL
PORTIONS OF LOT 14182 CHARLESHILL
VIDE DIAGRAM DSM NO. 1243/2026 ANNEXED TO
SITUATE AT CHARLESHILL IN THE GHANZI TRIBAL AREA
SCALE 1:1000

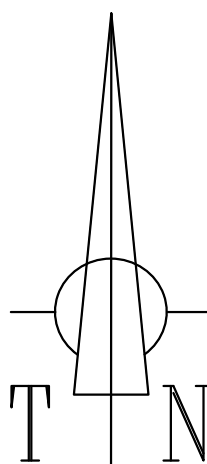


DSM No: 1244/2026

Approved

Director of Surveys and Mapping

Surveyed in February 2026

By me G.G. SESINYI
Land Surveyor

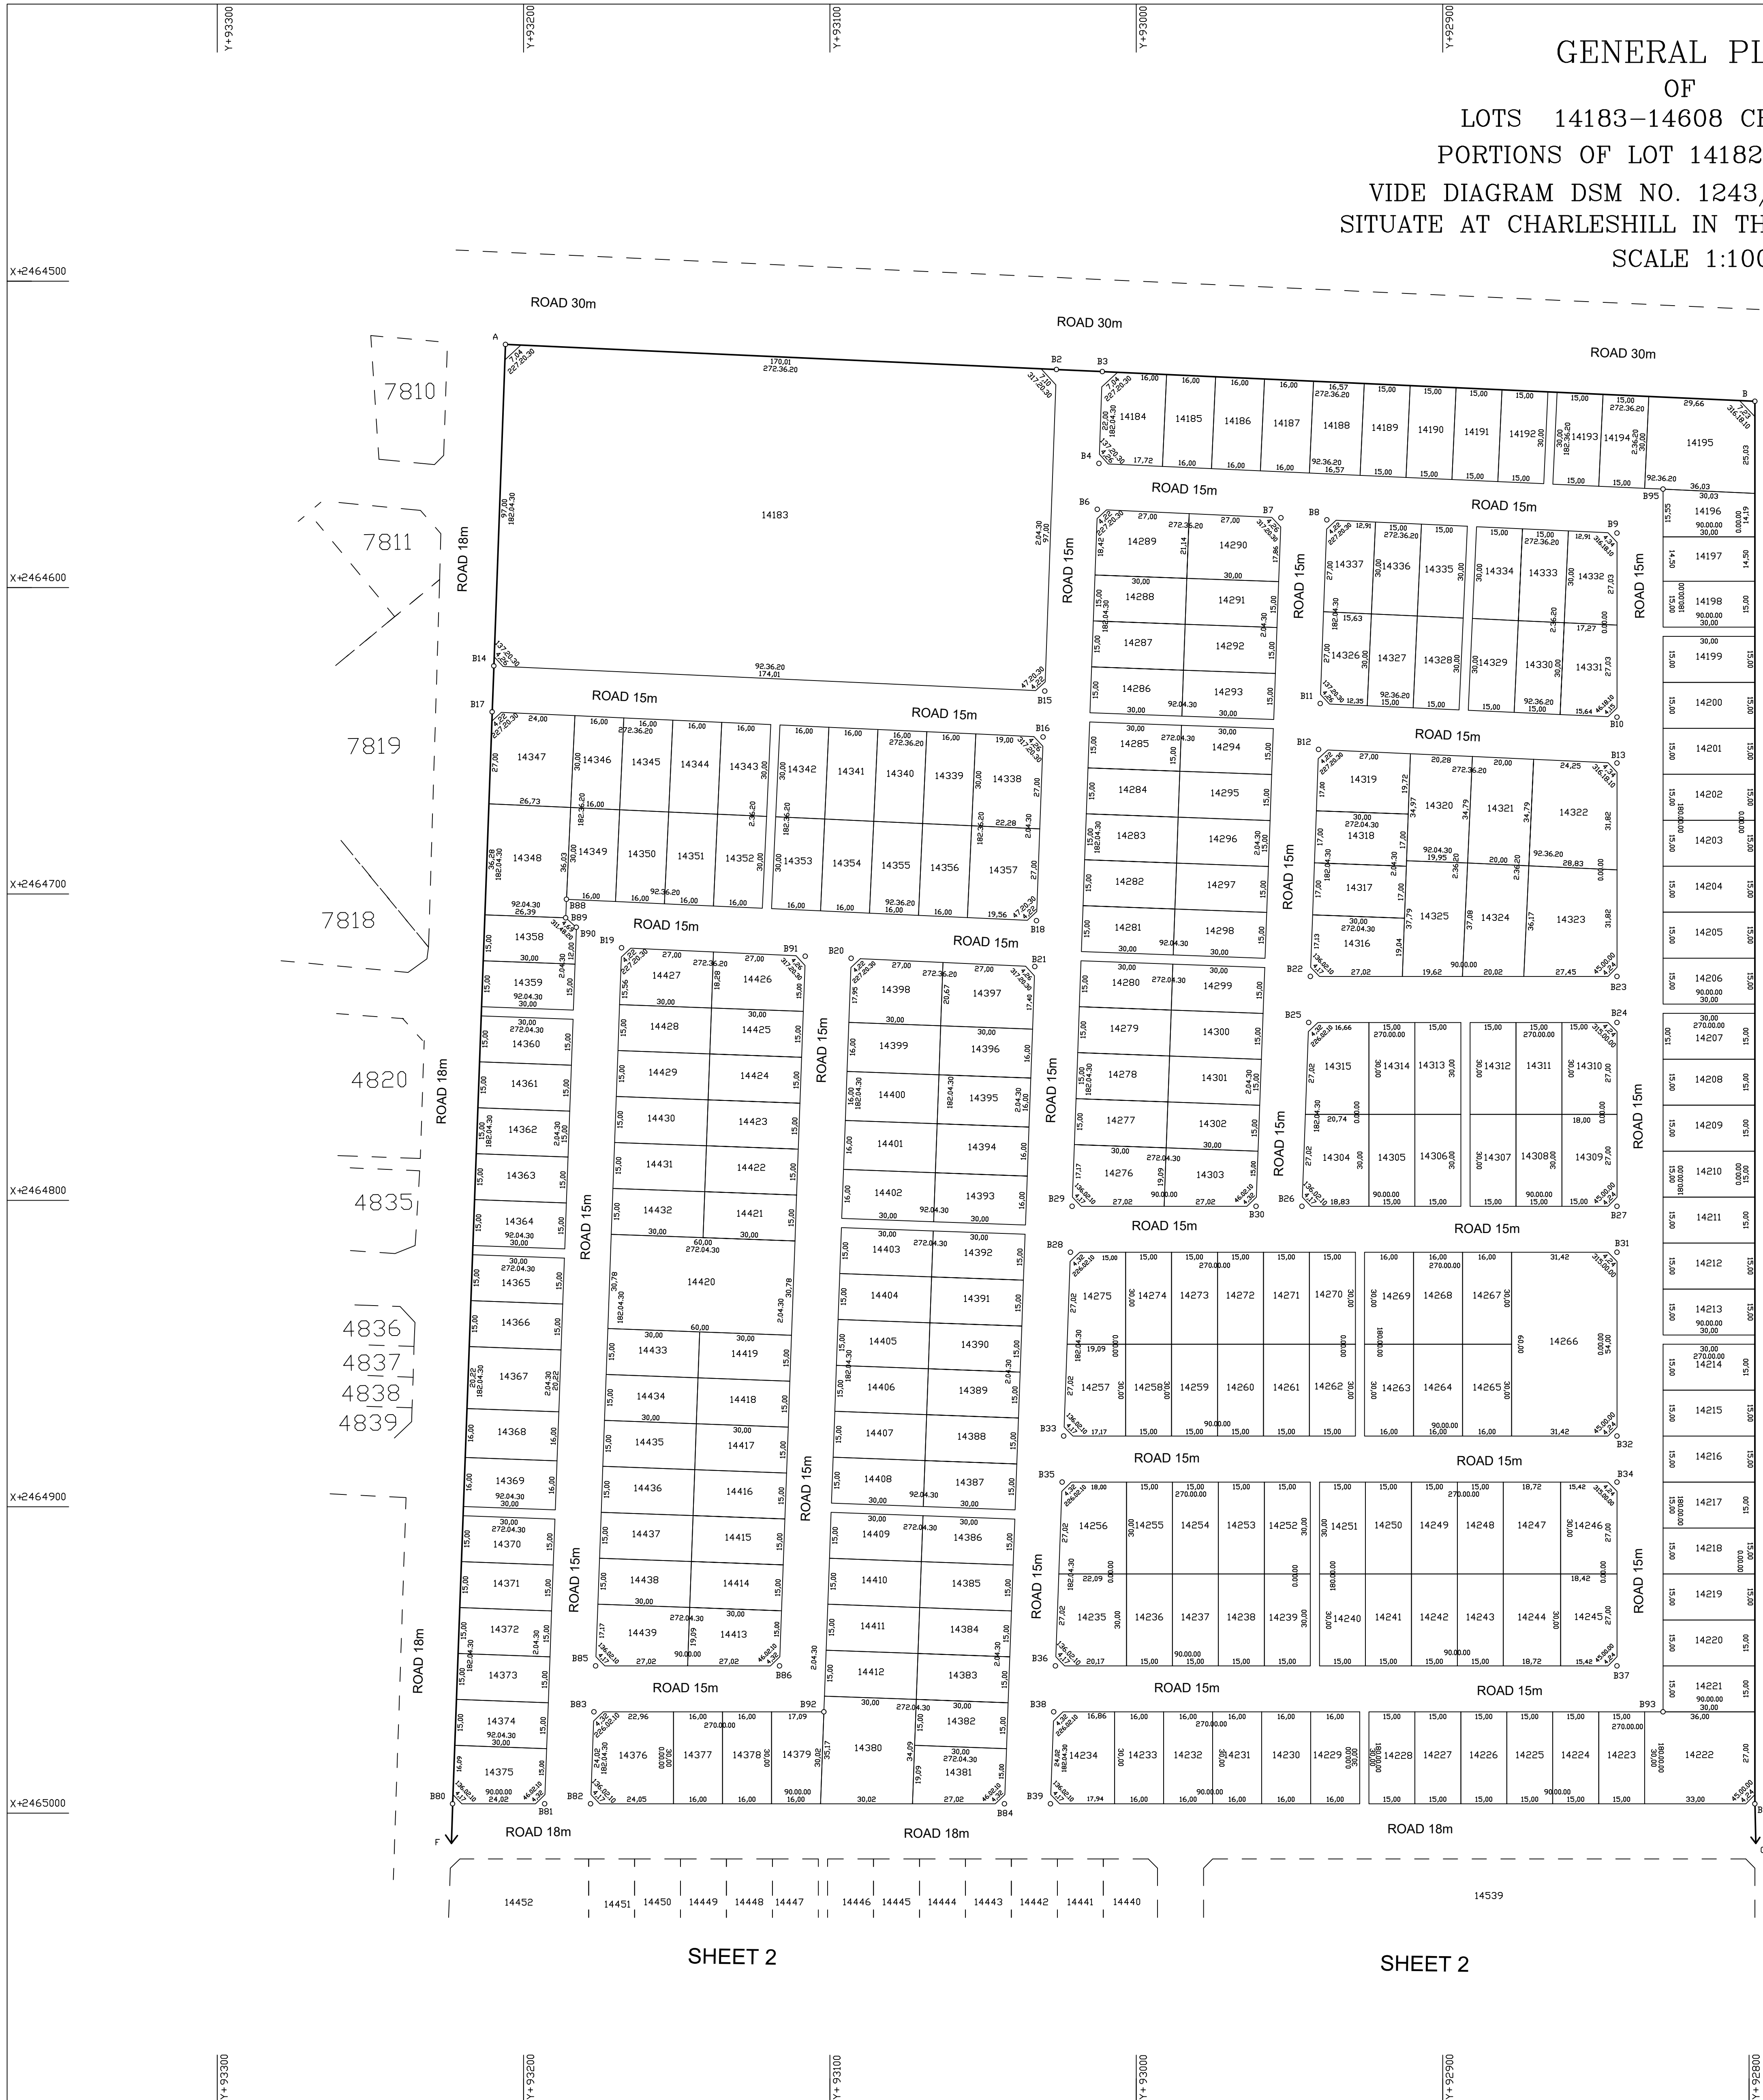

SHEET INDEX

SHEET 1: Lots 14183-14439

SHEET 2: Lots 14440-14608

BEACON DESCRIPTION

ALL: 12MM IRON PEG

SPLAY INFORMATION

A,B,B2,B3: 5m

All Others: 3m

PED WAY

All: 3m

BLOCK CORNER TABLE			
SYSTEM L.O. 21* CO-ORDINATES (metres)			
CONSTANTS	+	0,00	+
A	+ 93 205,88	+ 2 464 520,65	
B	+ 92 798,07	+ 2 464 520,65	
B1	+ 93 026,06	+ 2 464 520,65	
B2	+ 93 011,08	+ 2 464 520,65	
B3	+ 93 011,15	+ 2 464 520,65	
B4	+ 93 011,15	+ 2 464 520,65	
AB	408,24	272,36,20	A + 93 205,88 + 2 464 520,65
BC	831,43	0,00,00	B + 92 798,07 + 2 464 520,65
CD	583,80	80,00,00	C + 92 798,07 + 2 465 370,65
DE	137,81	122,13,20	D + 93 181,87 + 2 465 370,65
EF	128,23	212,13,20	E + 93 208,45 + 2 465 297,17
FA	668,48	182,04,30	F + 93 230,08 + 2 465 188,69
TOTAL AREA = 35,9794 Ha			

LOT AREAS			
LOT NUMBERS	SO METRES	LOT NUMBERS	SO METRES
14183	1,884,78	14314	450
14184	480	14315	450
14185	480	14316	450
14186	480	14317	450
14187	480	14318	450
14188	480	14319	450
14189	450	14320	702
14190	450	14321	450
14191	450	14322	971
14192	450	14323	1,047
14193	450	14324	736
14194	450	14325	450
14195	448	14326	450
14196	450	14327	450
14197	450	14328	450
14198	450	14329	450
14199	450	14330	450
14200	450	14331	450
14201	450	14332	450
14202	450	14333	450
14203	450	14334	450
14204	450	14335	450
14205	450	14336	450
14206	450	14337	450
14207	450	14338	450
14208	450	14339	450
14209	450	14340	480
14210	450	14341	450
14211	450	14342	450
14212	450	14343	450
14213	450	14344	450
14214	450	14345	450
14215	450	14346	450
14216	450	14347	861
14217	450	14348	902
14218	450	14349	480
14219	450	14350	450
14220	450	14351	450
14221	450	14352	450
14222	118	14353	450
14223	450	14354	450
14224	450	14355	450
14225	450	14356	450
14226	450	14357	450
14227	450	14358	450
14228	450	14359	450
14229	450	14360	450
14230	480	14361	450
14231	480	14362	450
14232	480	14363	450
14233	480	14364	450
14234	693	14365	450
14235	674	14366	450
14236	450	14367	60
14237	450	14368	450
14238	450	14369	450
14239	450	14370	450
14240	450	14371	450
14241	450	14372	450
14242	450	14373	450
14243	450	14374	450
14244	450	14375	450
14245	548	14376	786
14246	450	14377	450
14247	450	14378	450
14248	450	14379	450
14249	450	14380	450
14250	450	14381	450
14251	450	14382	450
14252	450	14383	450
14253	450	14384	450
14254	450	14385	450
14255	450	14386	450
14256	450	14387	450
14257	450	14388	450
14258	564	14389	450
14259	450	14390	450
14260	450	14391	450
14261	450	14392	450
14262	450	14393	450
14263	450	14394	450
14264	450	14395	450
14265	450	14396	450
14266	450	14397	450
14267	450	14398	450
14268	450	14399	450
14269	450	14400	450
14270	450	14401	450
14271	450	14402	450
14272	450	14403	450
14273	450	14404	450
14274	450	14405	450
14275	450	14406	450
14276	450	14407	450
14277	450	14408	450
14278	450	14409	450
14279	450	14410	450
14280	450	14411	450
14281	450	14412	450
14282	450	14413	450
14283	450	14414	450
14284	450	14415	450
14285	450	14416	450
14286	450	14417	450
14287	450	14418	450
14288	450	14419	450
14289	450	14420	450
14290	450	14421	142
14291	450	14422	450
14292	450	14423	450
14293	450	14424	450
14294	450	14425	450
14295	450	14426	450
14296	450	14427	450
14297	450	14428	450
14298	450	14429	450
14299	450	14430	450
14300	450	14431	450
14301	450	14432	450
14302	450	14433	450
14303	450	14434	450
14304	450	14435	450
14305	450	14436	450
14306	450	14437	450
14307	450	14438	450
14308	450	14439	584
14309	450		
14310	450		
